




TEL: 876 817 3220
EMAIL: draftingsolutions876@gmail.com

NOTES

Mechanical Equipment Schedule	
Type Mark	Description
AHU	Air Handling Unit - Split System -Horizontal : 36,000 Btu
CON	Condensing Unit - Air Cooled : 3Tons
EX -FAN	Exhauster with cabinet - ceiling mounted - 6" diameter

Air Terminal Schedule			
Type Mark	System Type	Description	Size
RD	Return Air	Return Diffuser - ceiling mounted	18"x18"
SD	Supply Air	Supply Register - floor mounted	12"x4"

MECHANICAL LEGEND

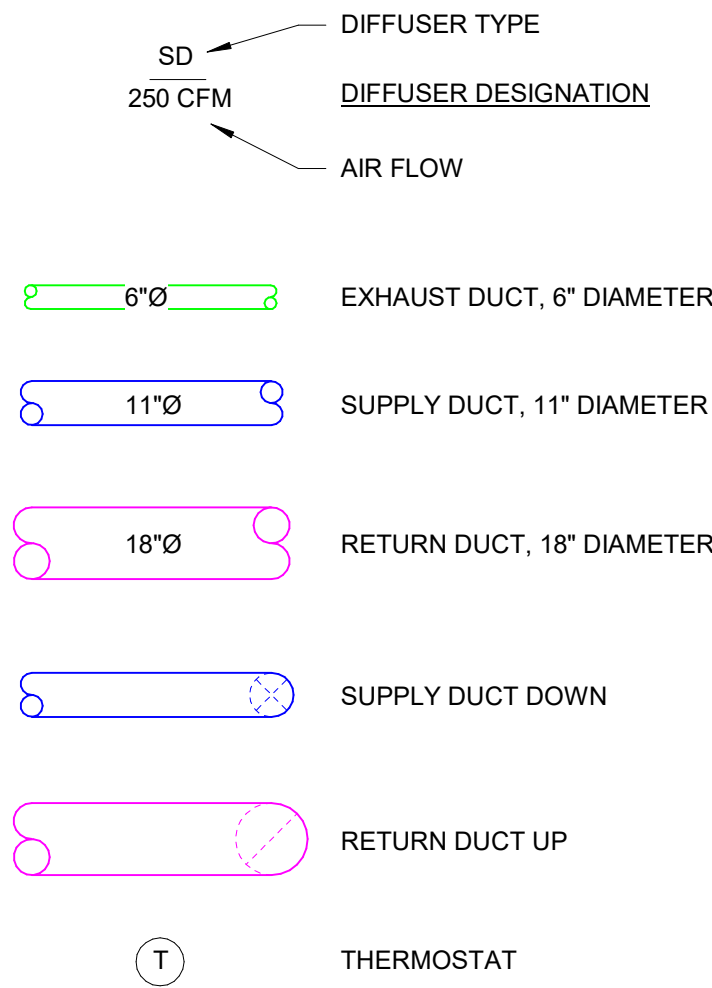[illegible]

CODE	SUITABILITY DESCRIPTION
STATUS	PURPOSE OF ISSUE

PROJECT

Project Name






TITLE

HVAC Plan

CLIENT

UPWORK

DRAWN BY AS	CHECKED BY KS	DATE DEC 2025
SCALE (@ A1) 1/4" = 1'-0"	PROJECT NUMBER 002	
DRAWING NUMBER M101		REV

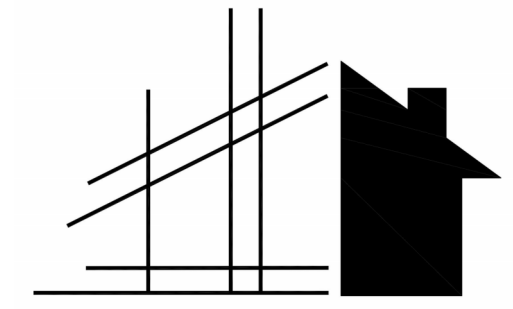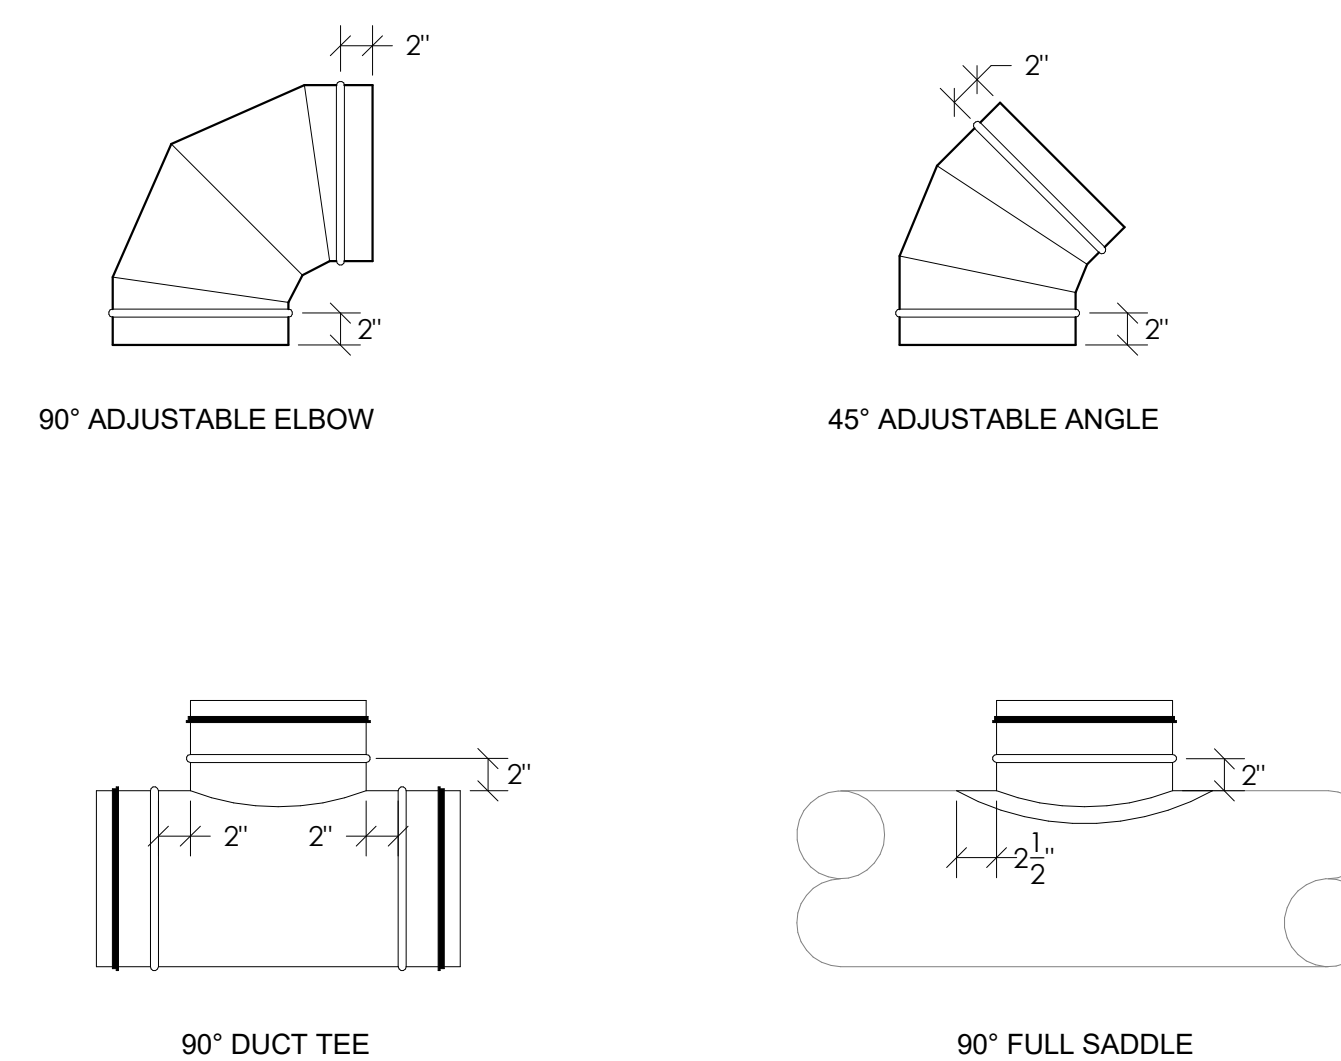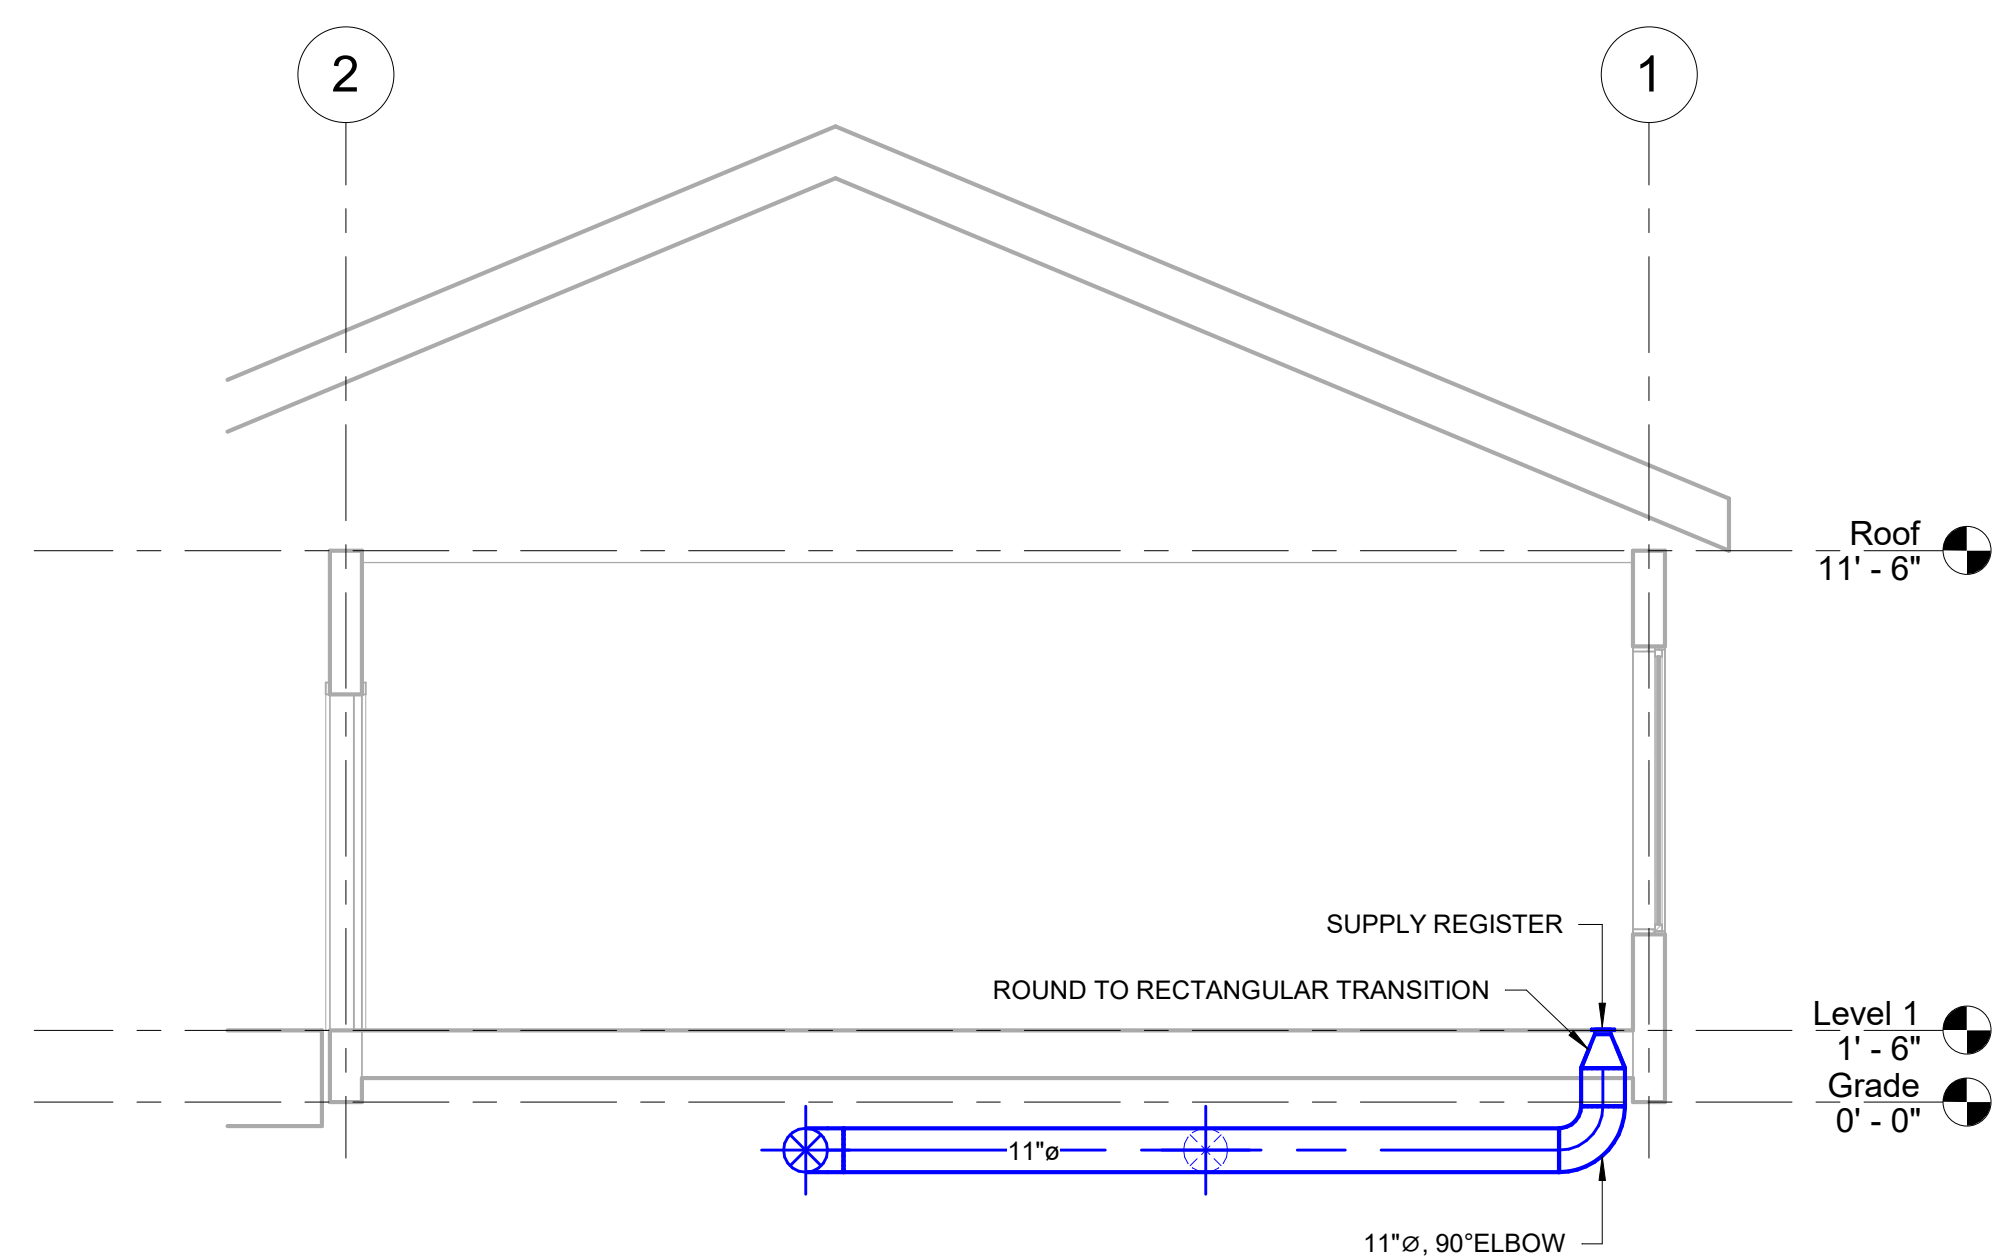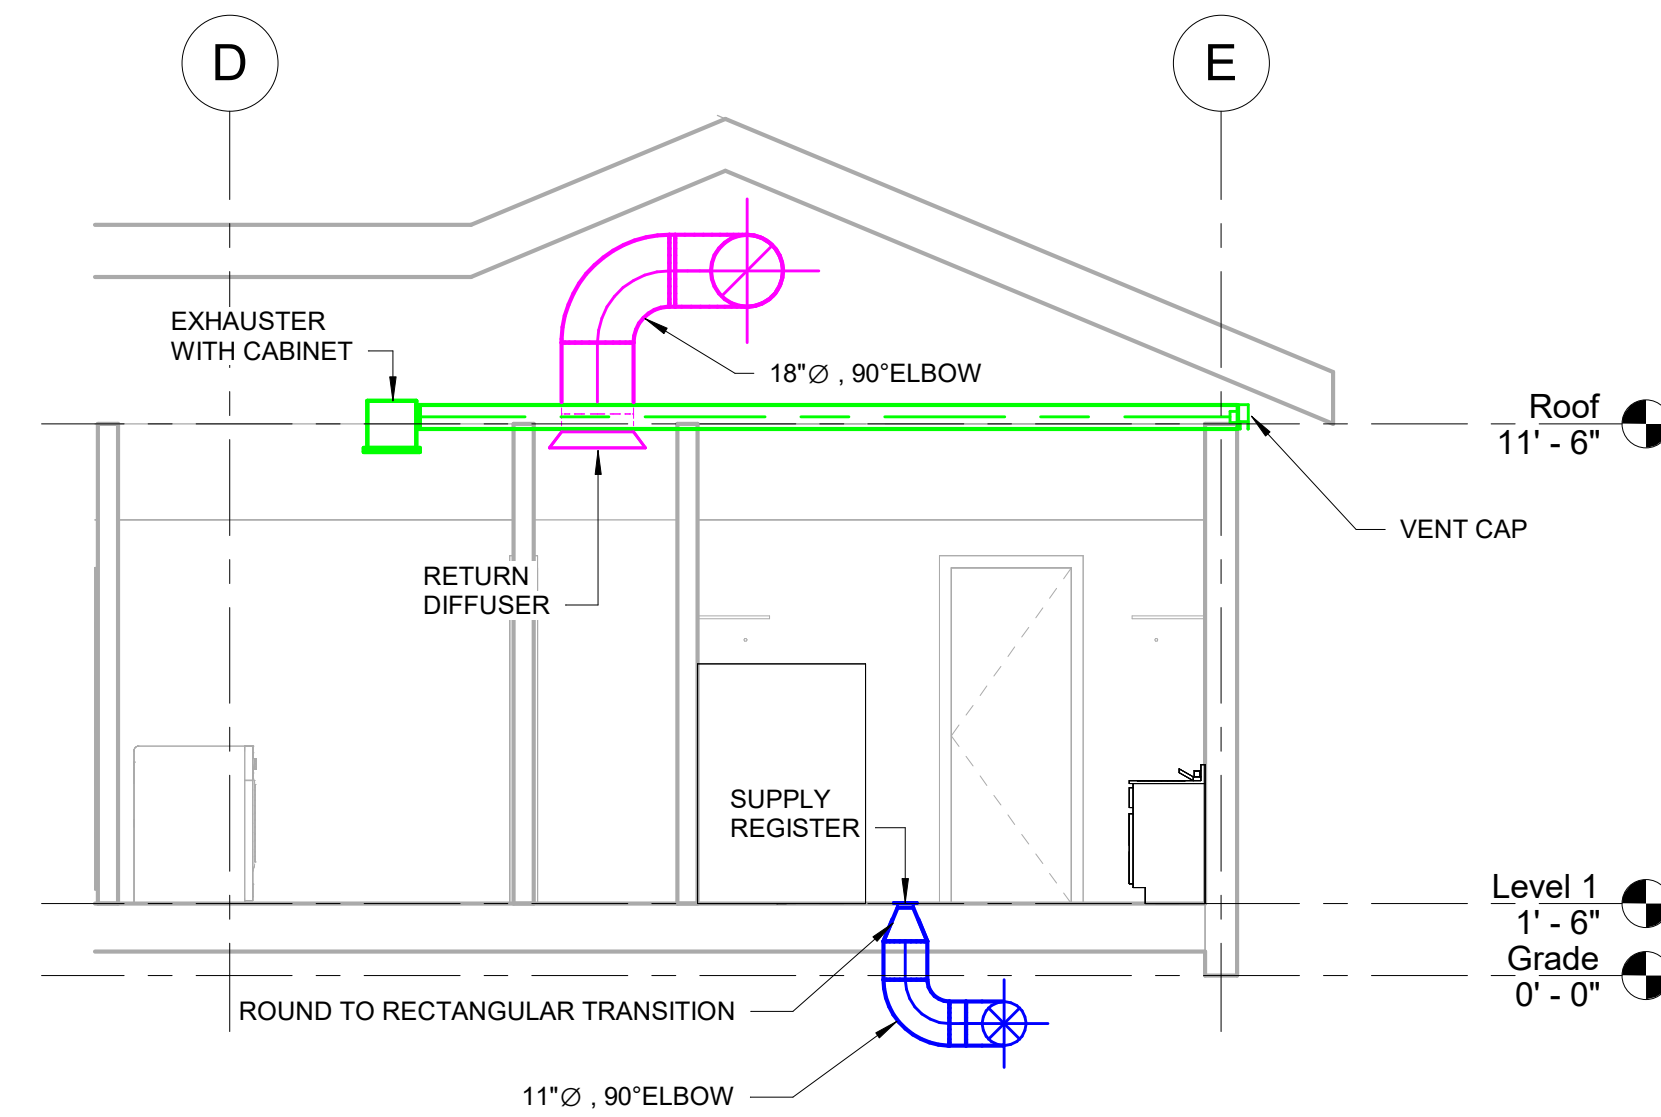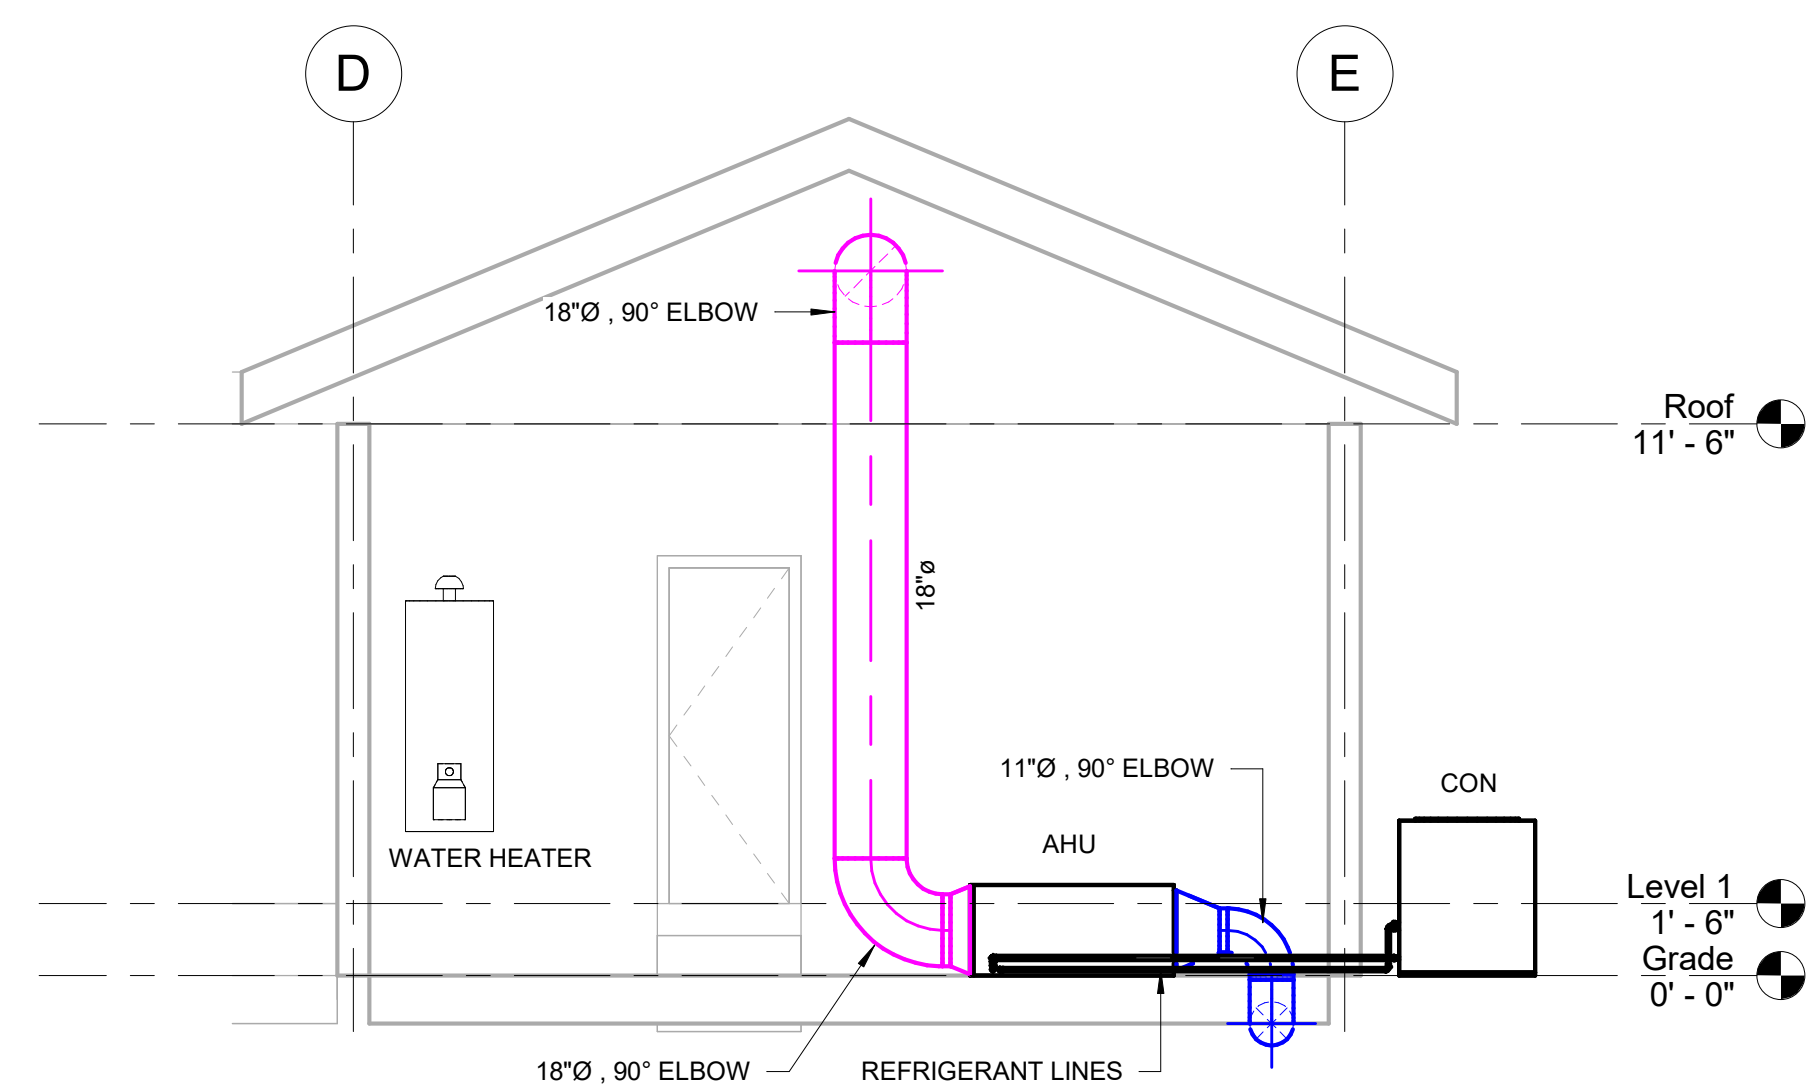

TEL: 876 817 3220
EMAIL: draftingsolutions876@gmail.com

NOTES

[illegible]

CODE	SUITABILITY DESCRIPTION
STATUS	PURPOSE OF ISSUE

PROJECT	
---------	--

Project Name



	TITLE
--	-------

HVAC sections

CLIENT

UPWORK

DRAWN BY Author	CHECKED BY Checker	DATE 12/14/25
SCALE (@ A1) As indicated	PROJECT NUMBER 002	
DRAWING NUMBER M102		REV

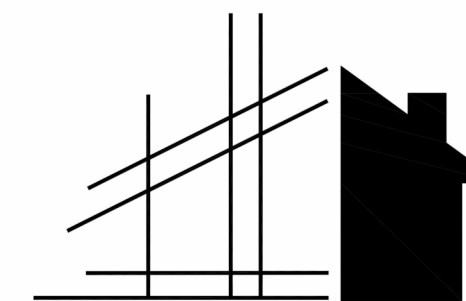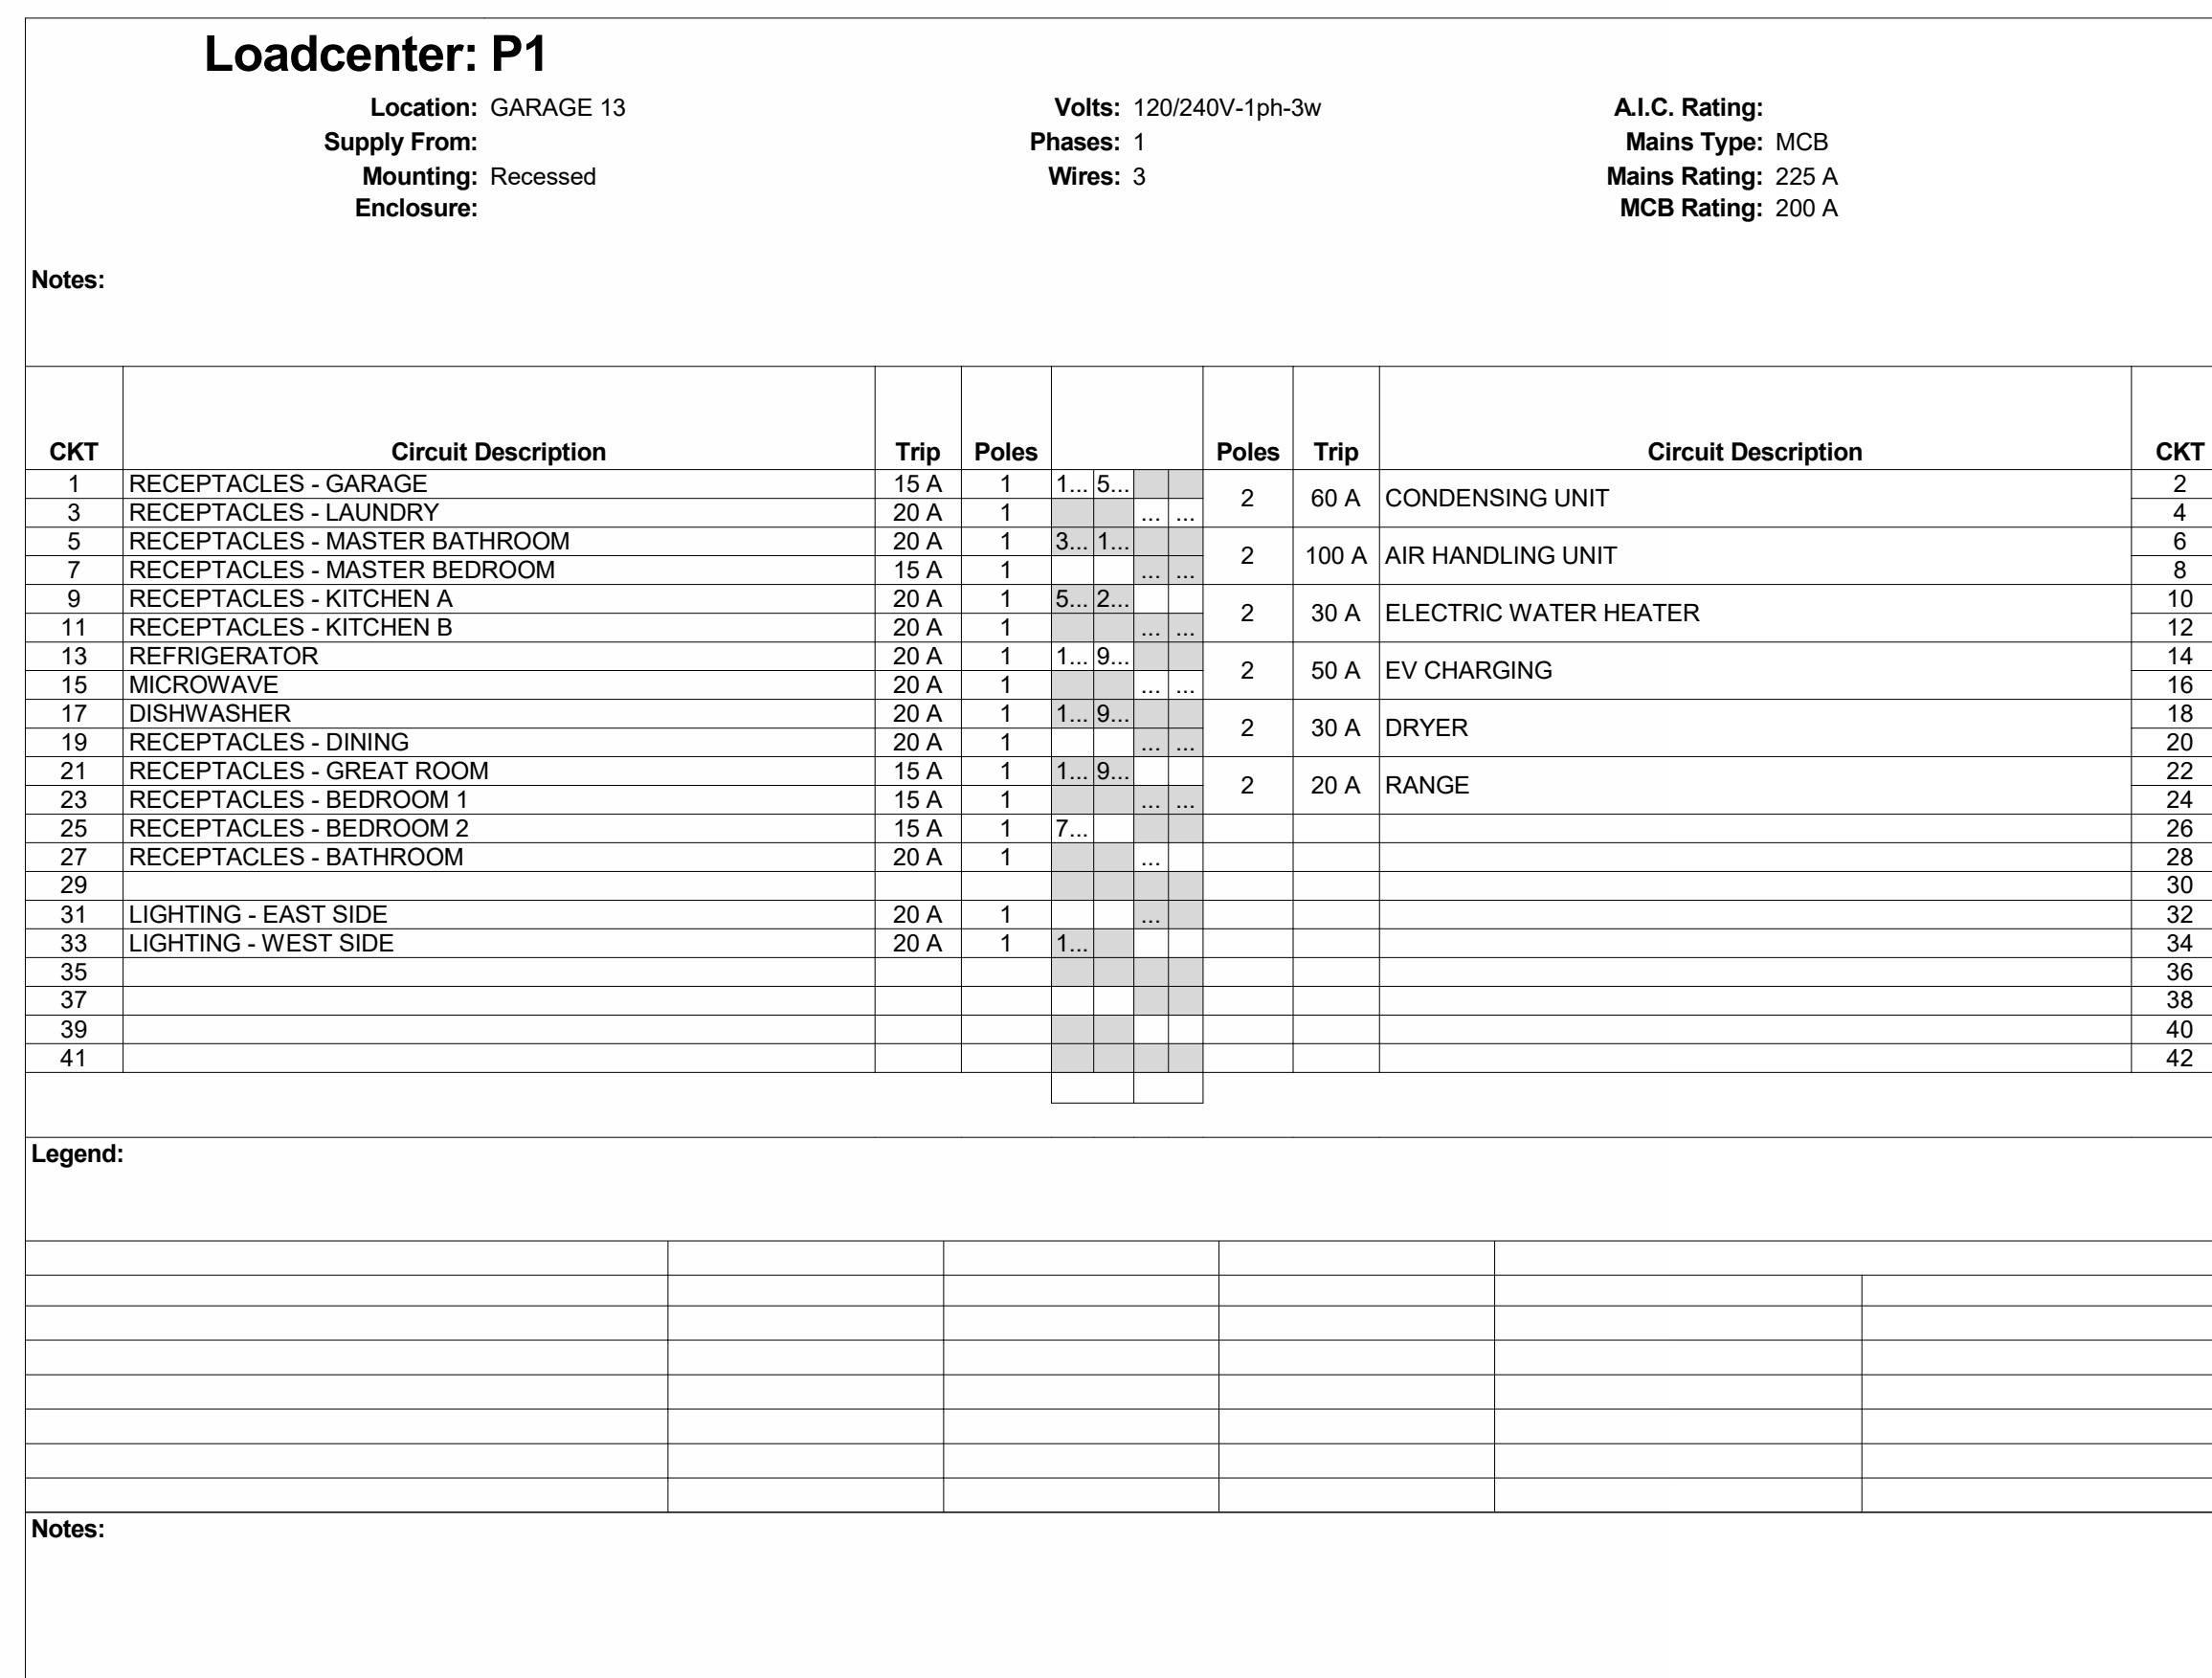

DRAFTING SOLUTIONS

TEL: 876 817 3220
EMAIL: draftingsolutions876@gmail.com

NOTES

[illegible]

CODE	SUITABILITY DESCRIPTION
STATUS	PURPOSE OF ISSUE

PROJECT

3-BEDROOM MEP

TITLE


Electrical Cover Sheet

CLIENT

UPWORK

DRAWN BY AS	CHECKED BY KS	DATE 12/06/25
SCALE (@ A1) 3/32" = 1'-0"	PROJECT NUMBER 003	
DRAWING NUMBER E100		REV


DRAWN BY Author	CHECKED BY Checker	DATE 12/06/25
SCALE (@ A1) As indicated	PROJECT NUMBER 003	
DRAWING NUMBER E101		F

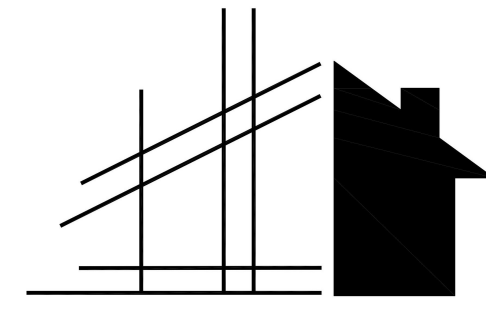

DRAFTING
SOLUTIONS

TEL: 876 817 3220
EMAIL: draftingolutions876@gmail.com

NOTES

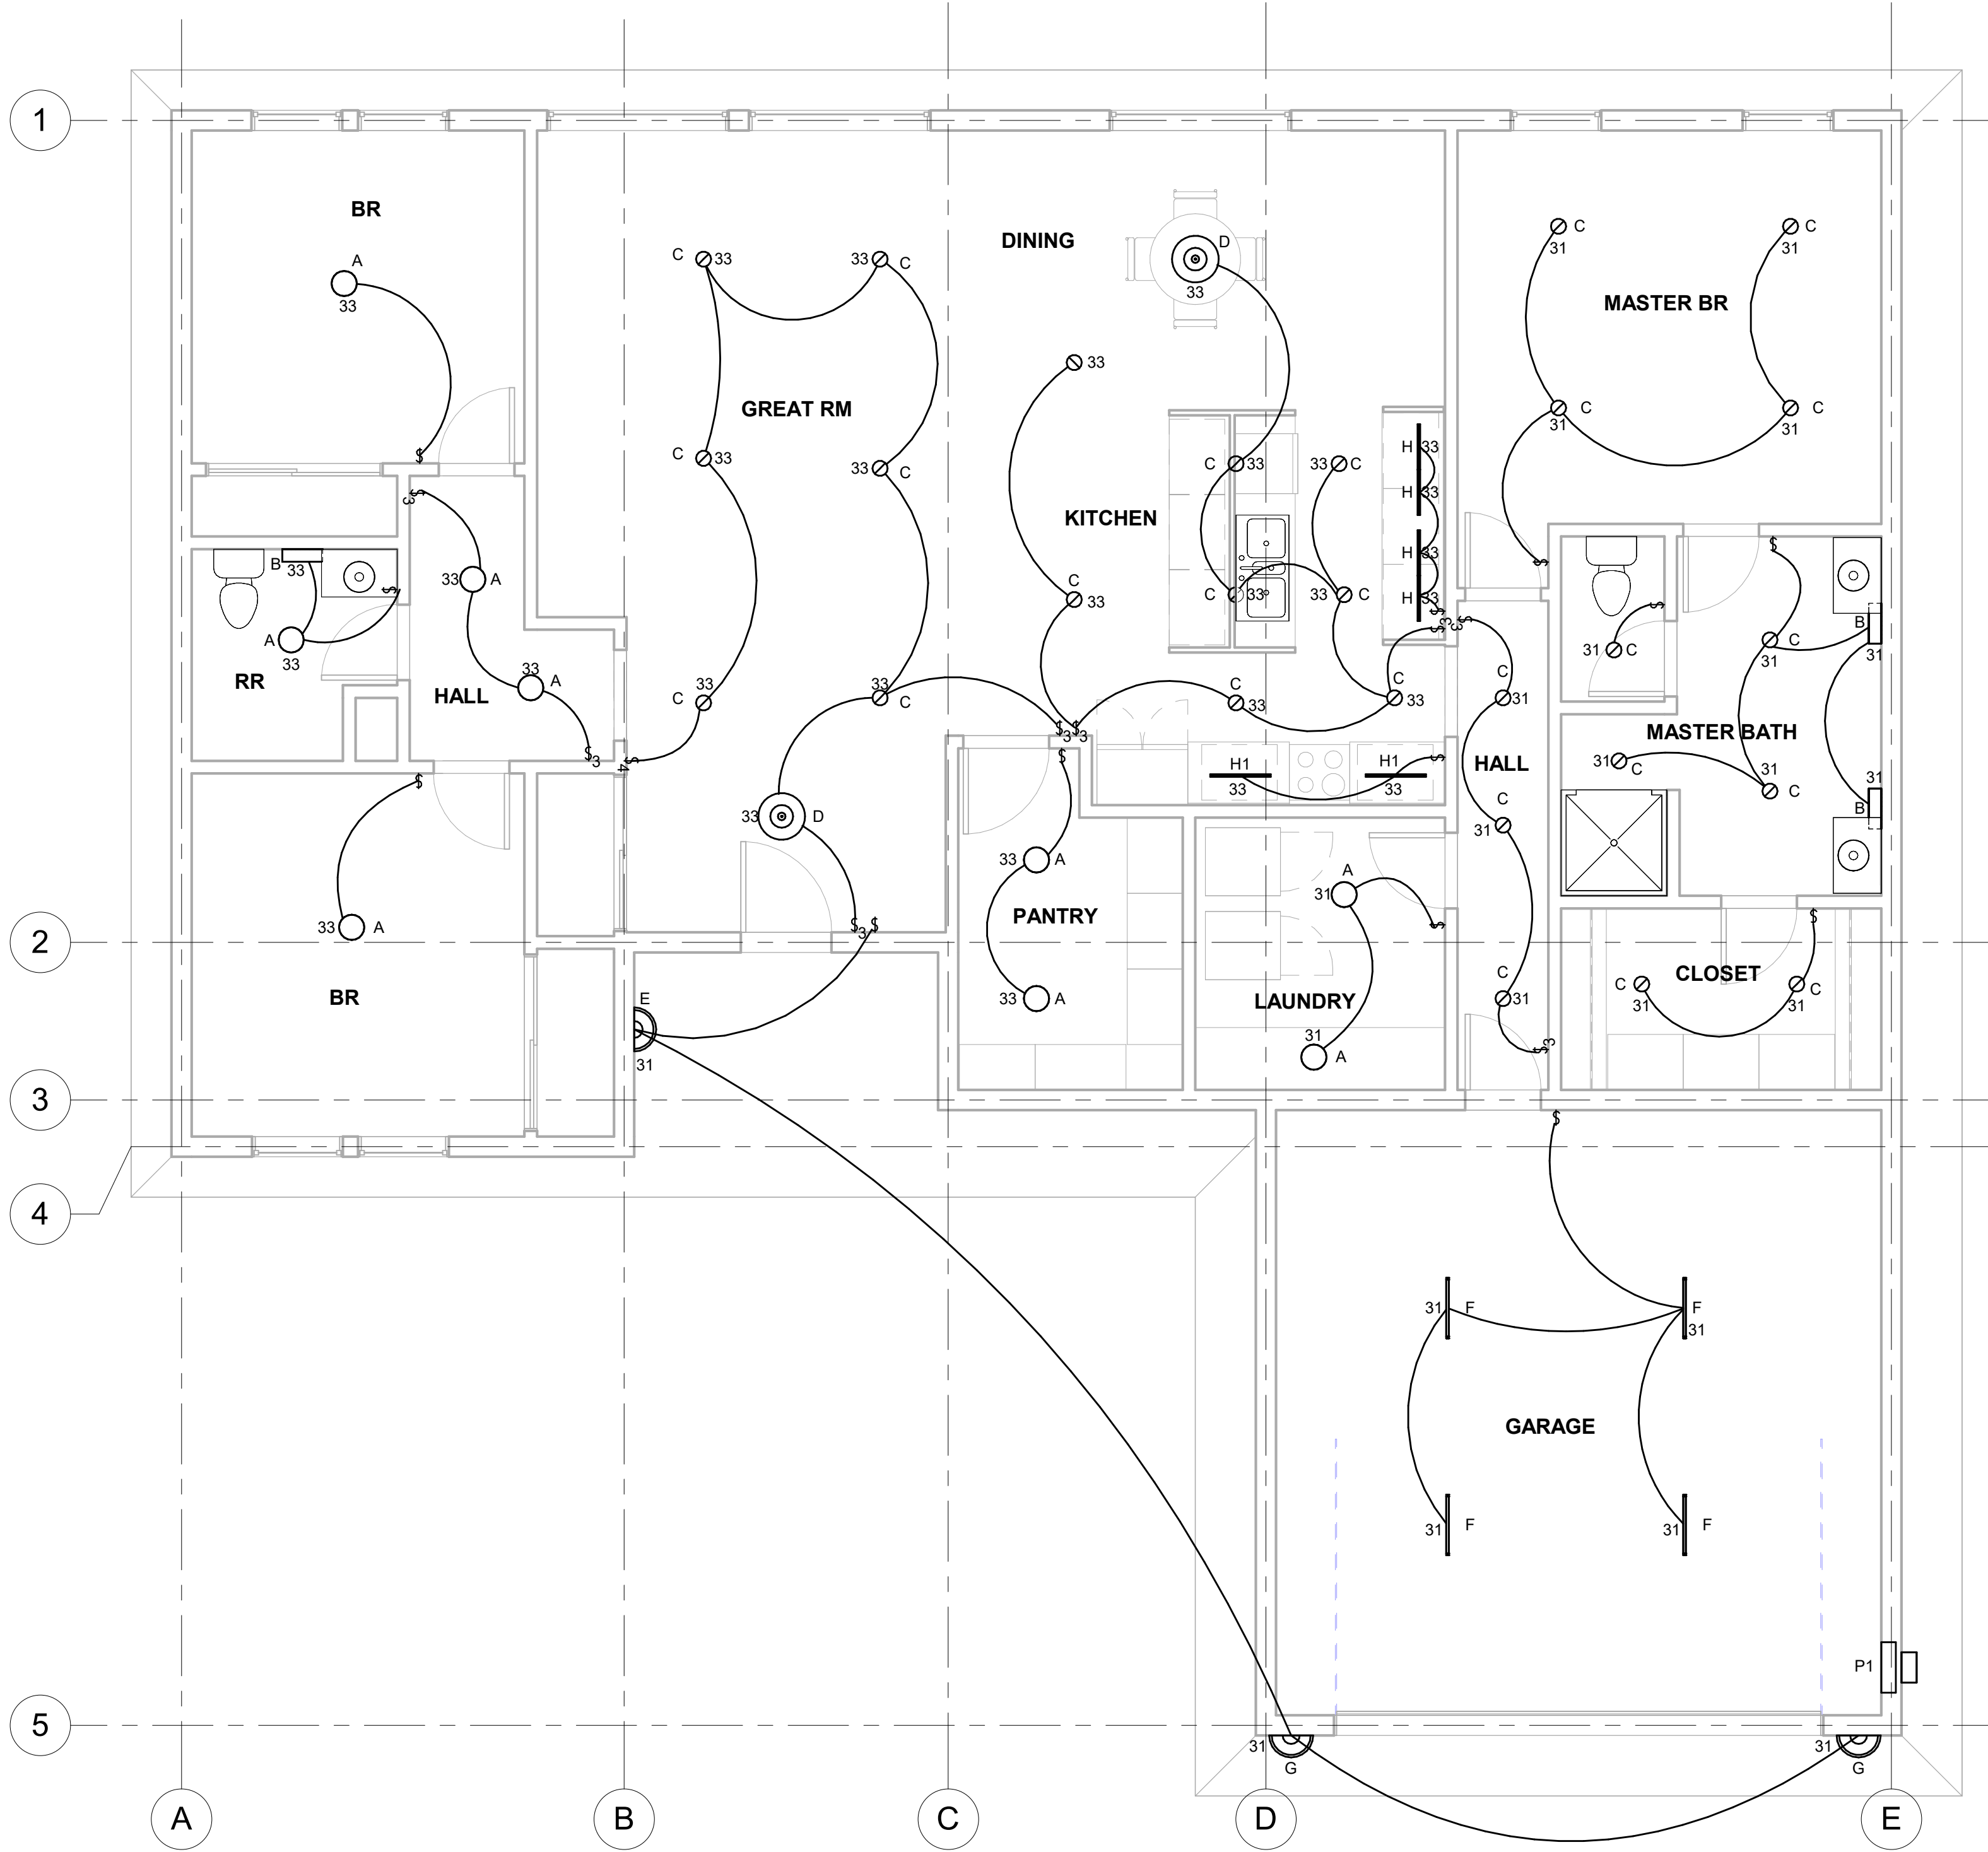

LIGHTING SYMBOLS

- \$ SINGLE POLE SWITCH
- \$₃ THREE WAY SWITCH
- \$₄ FOUR WAY SWITCH
- 31 ○ SURFACE DRUM LIGHT
CONNECTED TO CIRCUIT NO. 31
- 31 ◐ RECESSED CAN LIGHT
CONNECTED TO CIRCUIT NO. 31
- 31 ◻ WALL SCONCE LIGHT - FLAT ROUND
CONNECTED TO CIRCUIT NO. 31
- 31 ◑ WALL SCONCE LIGHT - UPLIGHT
CONNECTED TO CIRCUIT NO. 31
- 33 ⊙ PENDANT LIGHT DISK
CONNECTED TO CIRCUIT NO. 33
- 33 — FLOURESCENT LIGHT
CONNECTED TO CIRCUIT NO. 33

Lighting Fixture Schedule			
Type Mark	Family	Electrical Data	Luminous Flux
A	Ceiling Light - Flat Round	120 V/1-15 VA	855 lm
B	Scnce Light - Flat Round	120 V/1-60 VA	855 lm
C	Downlight - Recessed Can	120 V/1-60 VA	855 lm
D	Pendant Light - Disk	120 V/1-100 VA	1690 lm
E	Scnce Light - Uplight	120 V/1-60 VA	855 lm
F	Downlight - Strip	120 V/1-17 VA	1350 lm
G	Scnce Light - Uplight	120 V/1-60 VA	855 lm
H	Downlight - Under Cabinet	120 V/1-8 VA	400 lm
H1	Downlight - Under Cabinet	120 V/1-8 VA	400 lm
S1	Street Light - Antique	120 V/1-250 VA	5000 lm

Rev	Description	Date

CODE	SUITABILITY DESCRIPTION
STATUS	PURPOSE OF ISSUE

PROJECT

3-BEDROOM MEP


TITLE

Lighting Floor Plan

CLIENT

UPWORK

DRAWN BY Author	CHECKED BY Checker	DATE 12/06/25
SCALE (@ A1) As indicated		PROJECT NUMBER 003
DRAWING NUMBER E102		REV

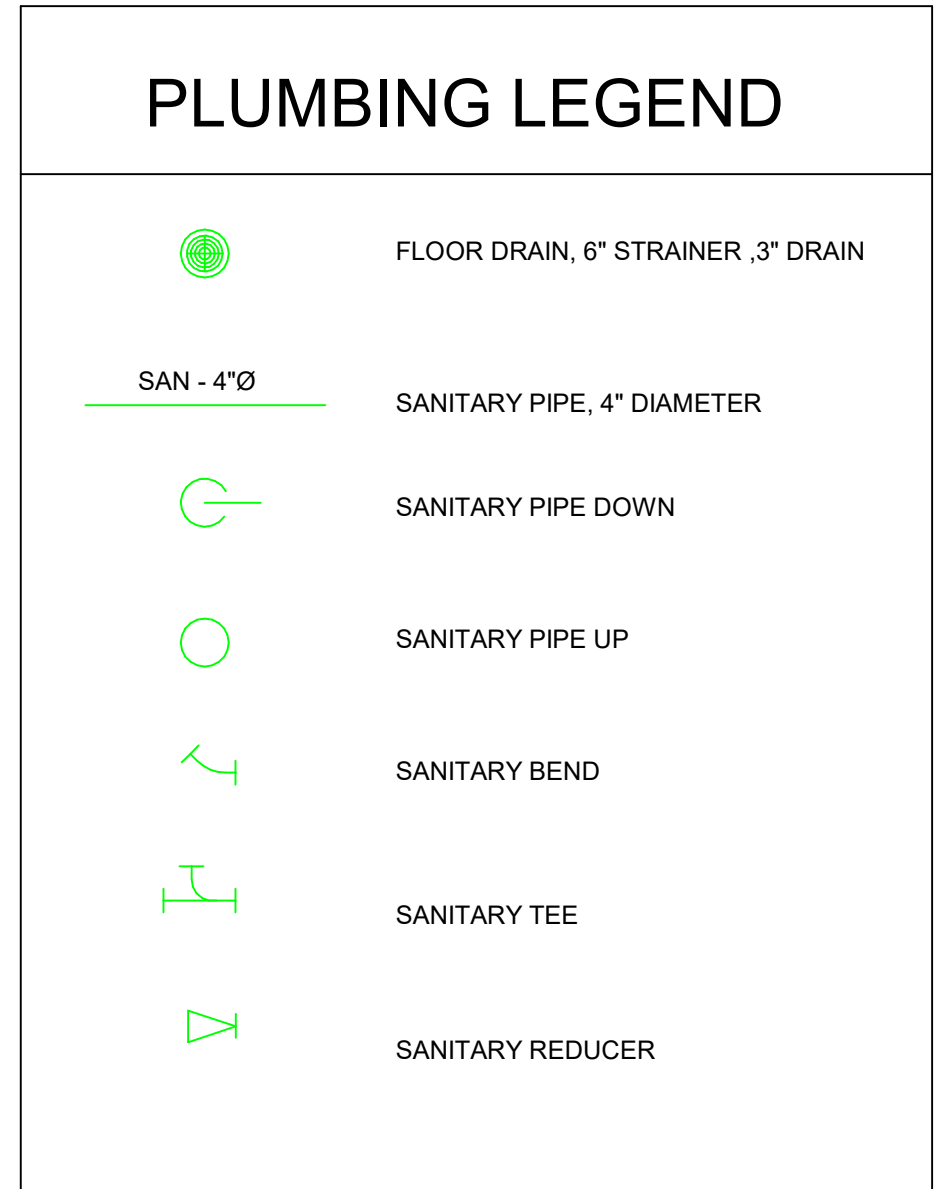

TEL: 876 817 3220
EMAIL: draftingsolutions876@gmail.com

NOTES

CODE	SUITABILITY DESCRIPTION
STATUS	PURPOSE OF ISSUE

PROJECT

Project Name


TITLE

Sanitary Plan

CLIENT

UPWORK

DRAWN BY Author	CHECKED BY Checker	DATE 01/02/26
SCALE (@ A1) 1/4" = 1'-0"	PROJECT NUMBER 002	
DRAWING NUMBER P101		REV

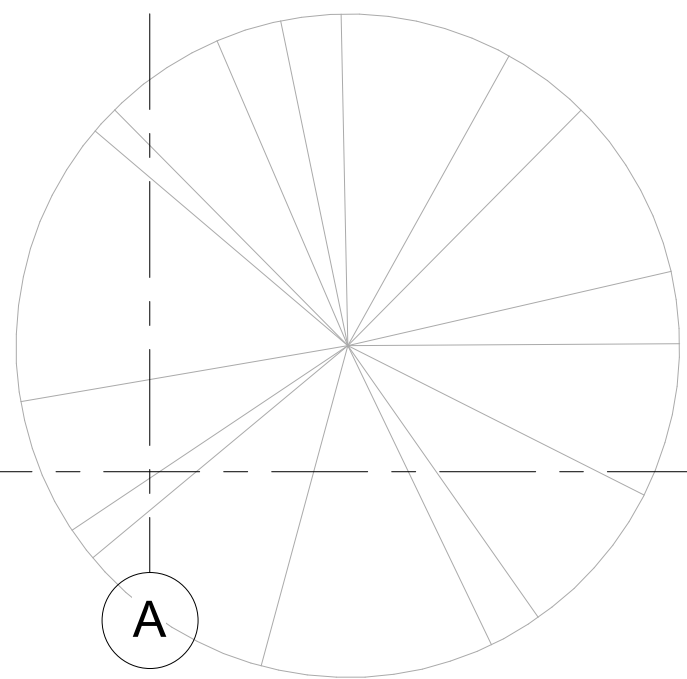

DCW - 1/2"Ø	DOMESTIC COLD WATER, 1/2" DIAMETER
DHW - 1/2"Ø	DOMESTIC HOT WATER, 1/2" DIAMETER
	DOMESTIC COLD WATER PIPE DOWN
	DOMESTIC COLD WATER PIPE UP
	DOMESTIC COLD WATER BEND
	DOMESTIC COLD WATER TEE
	DOMESTIC COLD WATER REDUCER



NOTES

CODE	SUITABILITY DESCRIPTION
STATUS	PURPOSE OF ISSUE

Project Name

Water Supply Plan

UPWORK

DRAWN BY Author	CHECKED BY Checker	DATE 01/04/26
SCALE (@ A1) 1/4" = 1'-0"		PROJECT NUMBER 002
DRAWING NUMBER P102		REV