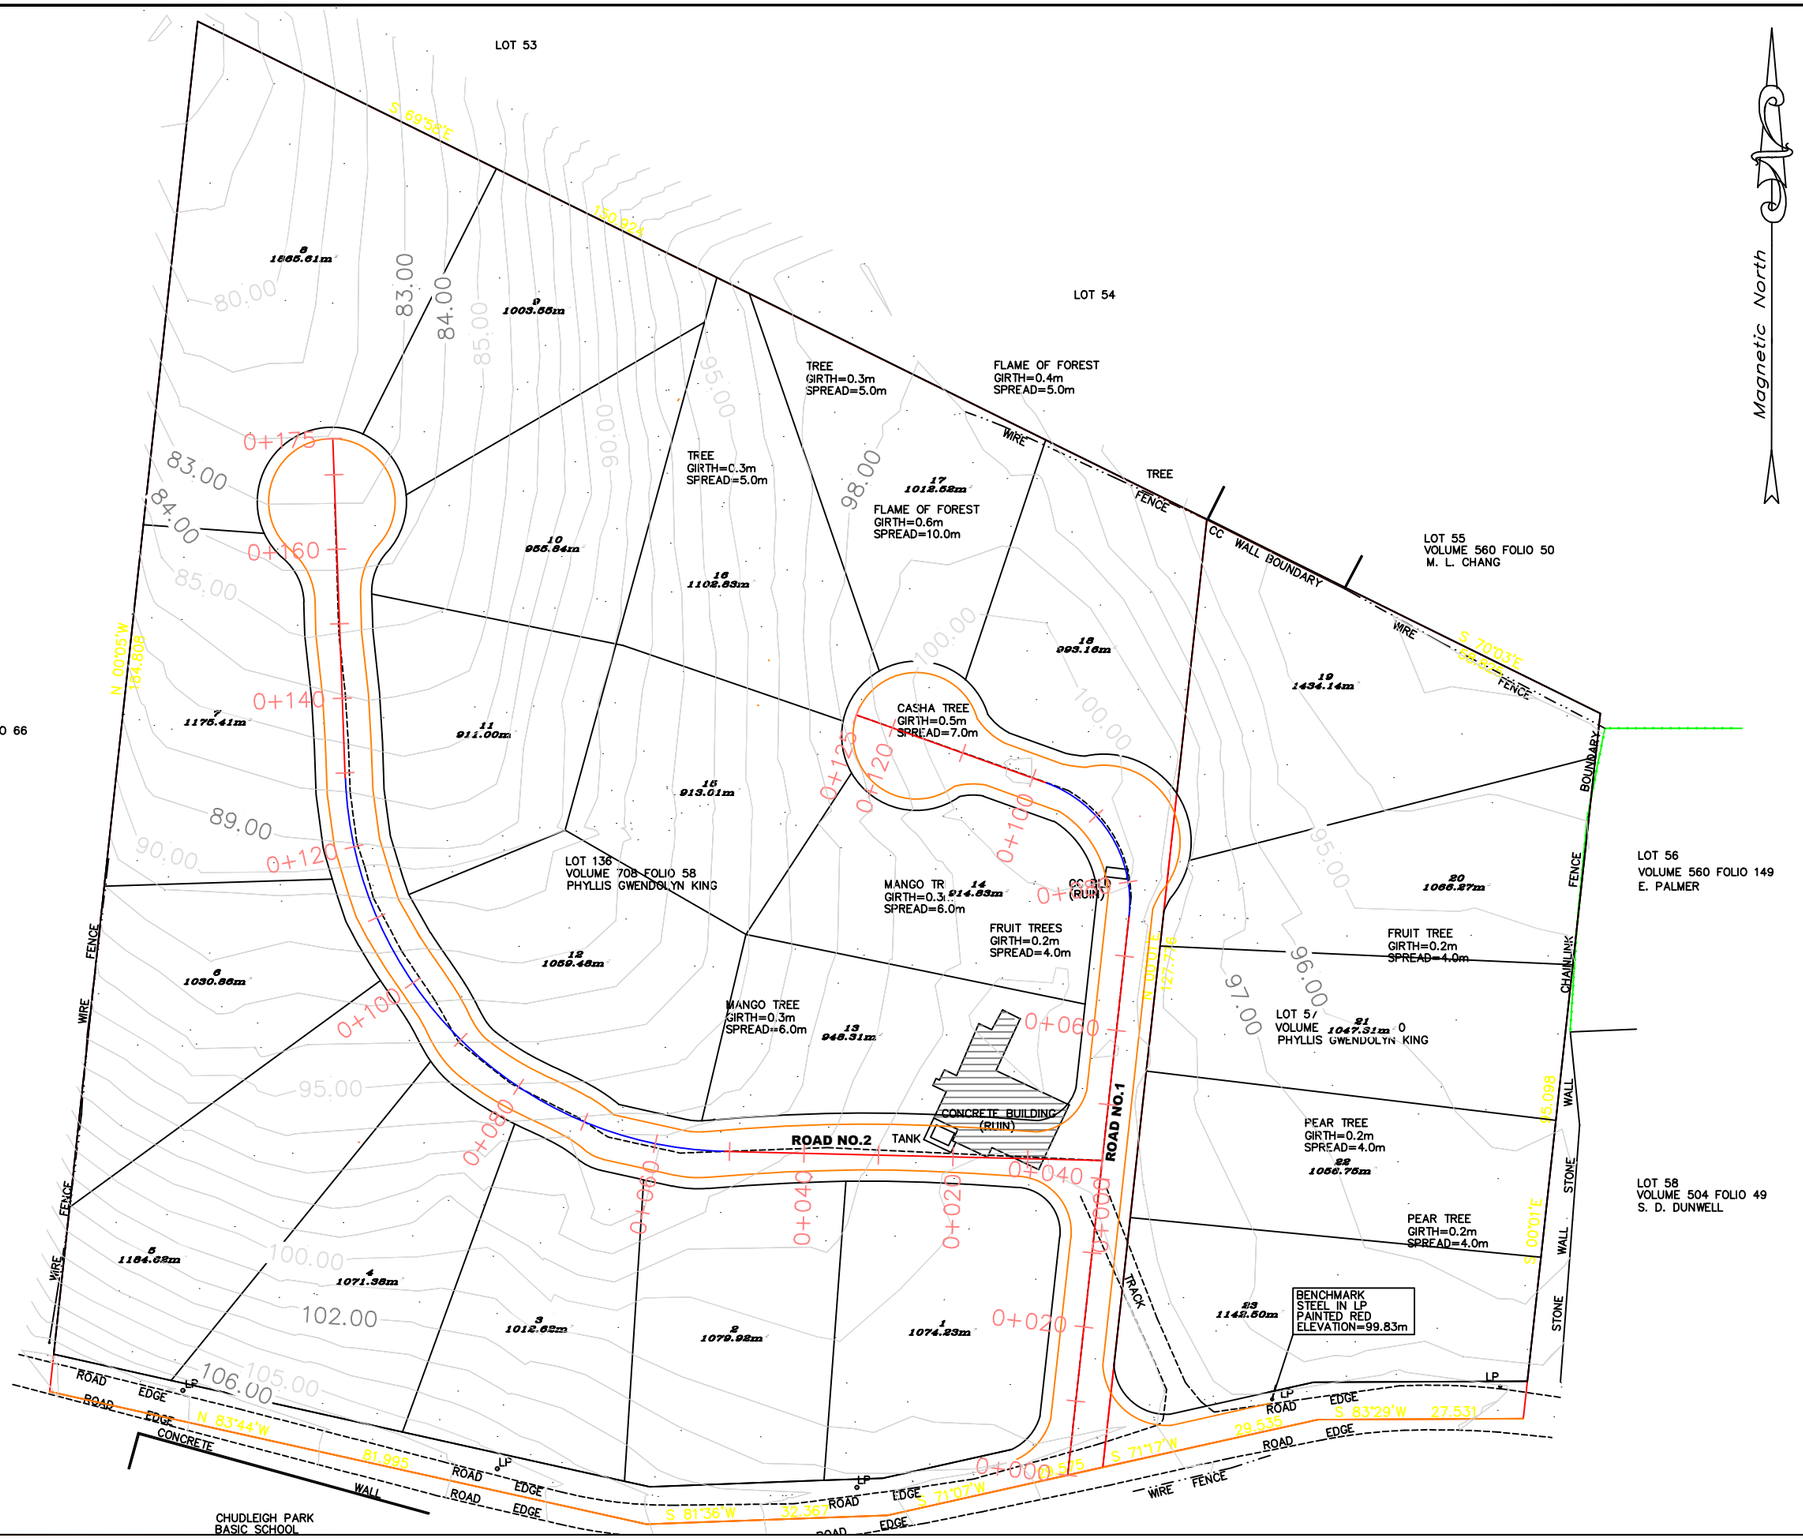

NOTES:

1. THE CONTRACTOR SHALL BE RESPONSIBLE FOR ACCURATELY SETTING OUT THE WORKS. ANY DISCREPANCIES MUST BE RESOLVED WITH THE CLIENT BEFORE PROCEEDING WITH THE CONSTRUCTION.

DRAFTING SOLUTIONS

PROJECT NAME:	Chudleigh, Manchester
DRAWING NAME:	Layout Plan
DATE: NOV 2024	REVISION NO: 00
SHEET NO: 01 OF 03	SCALE: -

Road No.1 PROFILE

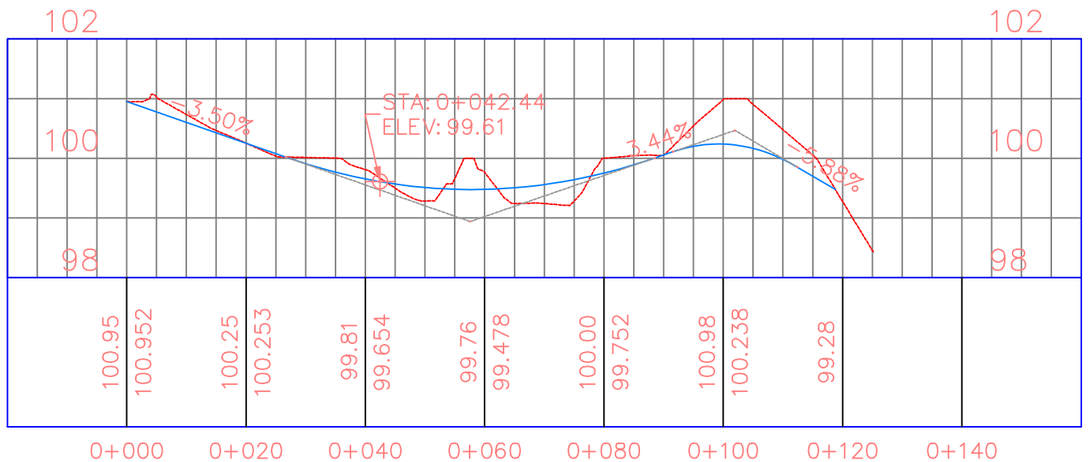

NOTES:

1. THE CONTRACTOR SHALL BE RESPONSIBLE FOR ACCURATELY SETTING OUT THE WORKS. ANY DISCREPANCIES MUST BE RESOLVED WITH THE CLIENT BEFORE PROCEEDING WITH THE CONSTRUCTION.

DRAFTING SOLUTIONS

PROJECT NAME:	Chudleigh, Manchester
DRAWING NAME:	Road No.1 Profile
DATE: NOV 2024	REVISION NO: 00
SHEET NO: 02 OF 03	SCALE: -

Road No.2 PROFILE

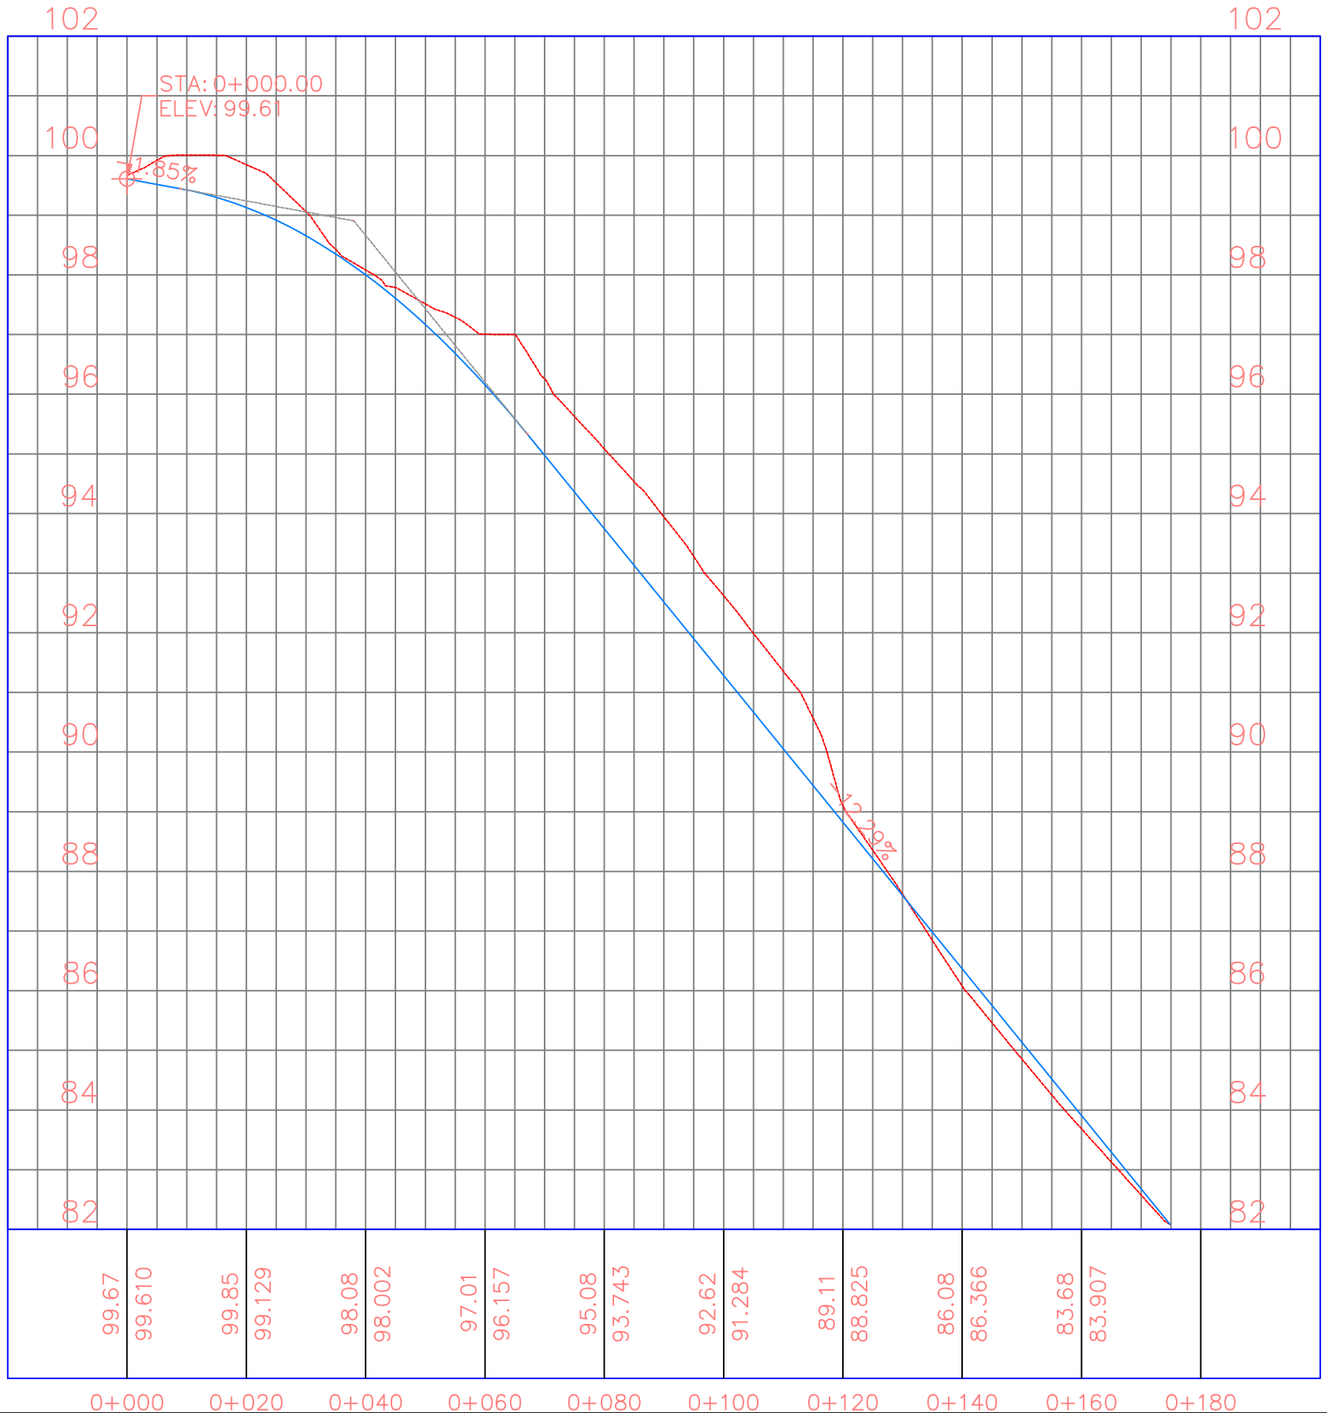

NOTES:

1. THE CONTRACTOR SHALL BE RESPONSIBLE FOR ACCURATELY SETTING OUT THE WORKS. ANY DISCREPANCIES MUST BE RESOLVED WITH THE CLIENT BEFORE PROCEEDING WITH THE CONSTRUCTION.

DRAFTING SOLUTIONS

PROJECT NAME:	Chudleigh, Manchester
DRAWING NAME:	Road No.2 Profile
DATE: NOV 2024	REVISION NO: 00
SHEET NO: 03 OF 03	SCALE: -